


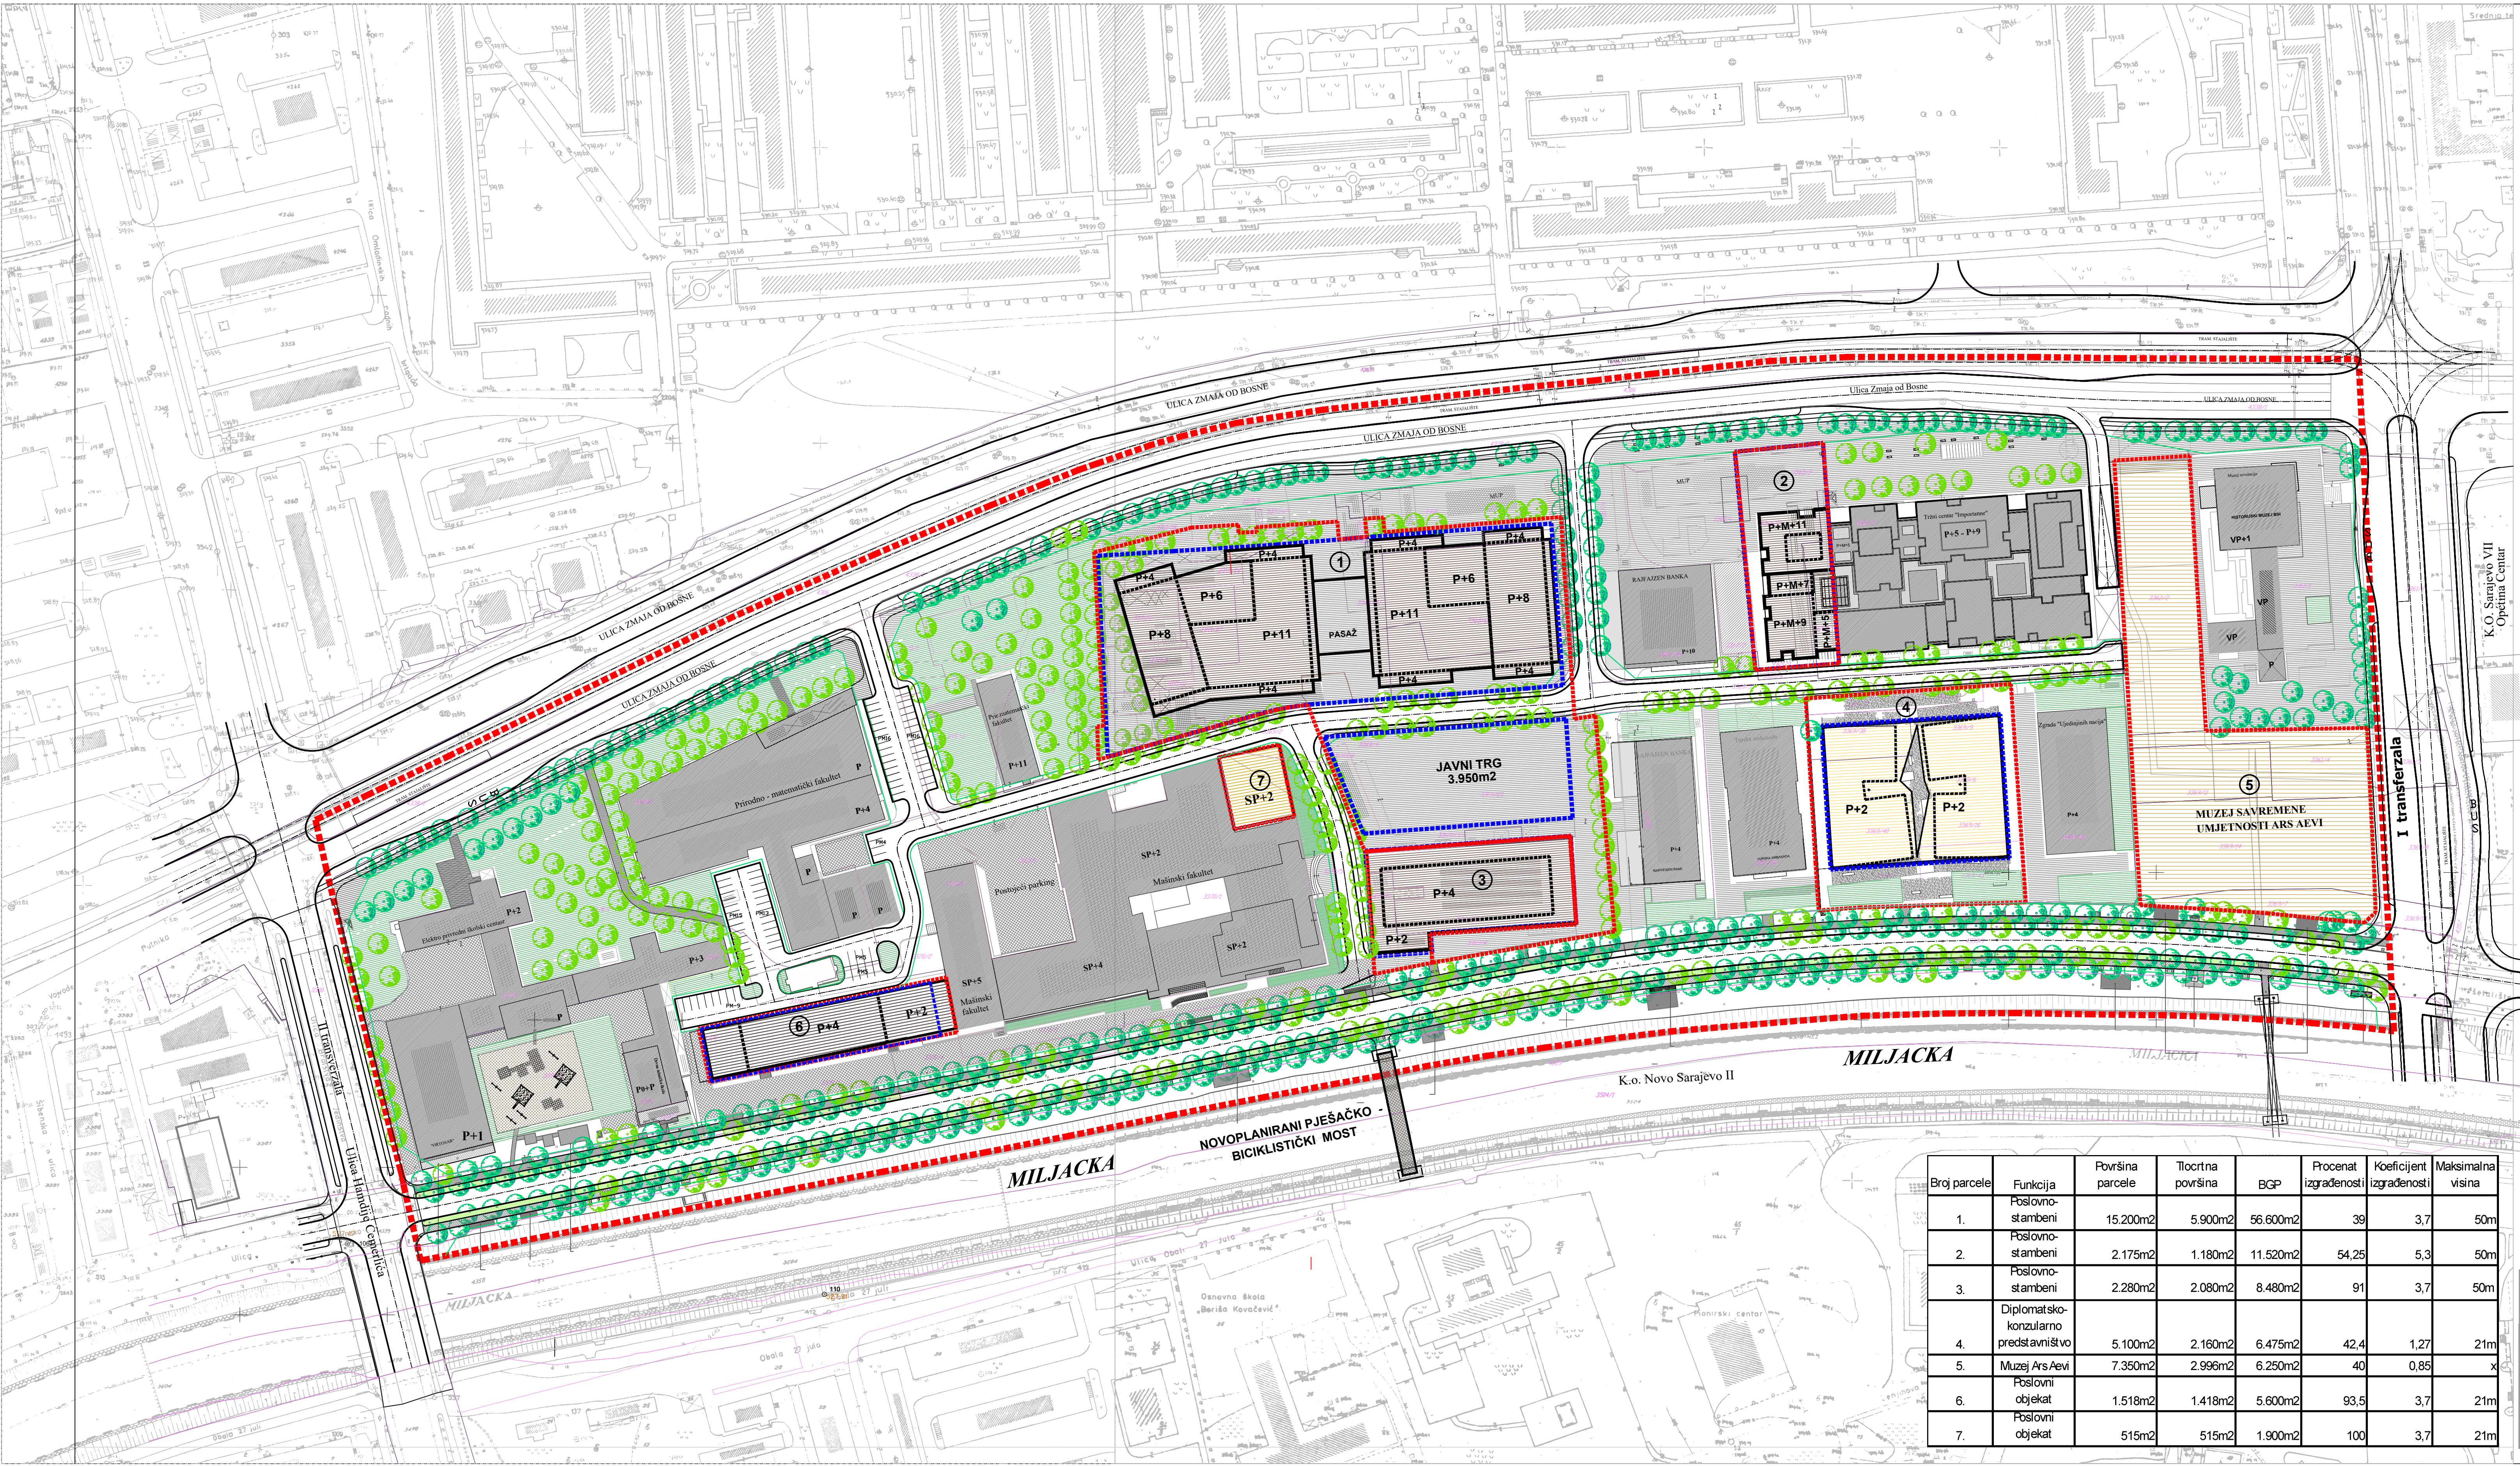

REGULACIONI PLAN
"KVADRANT C - MARIJIN DVOR"

PLANIRANO STANJE
RAZMJJEŠTAJ, NAMJENA I
SPRATNOST OBJEKATA M 1:1 000

- GRANICA OBUHVATA
- GRANICA KATASTARSKIH PARCELA
- REGULACIONA LINIJA GRAD.PARCELE
- MAX.GRADEVINSKA LINIJA OBJEKATA
- GRADEVINSKA LINIJA SPRATNIH ETAŽA
- GRADEVINSKA LINIJA PODZEMNIH ETAŽA
- MUZEJ SAVREMENE UMJETNOSTI ARS AEVI izuzeto iz režima zabrane građenja (Sl.Novine Kantona Sarajevo br. 51/18 i 15/19), (Rješenje odobrenja za građenje br. 08 -19 - 4718/23 od 19.08.2024)
- POSTOJEĆI OBJEKTI
- PLANIRANI POSLOVNO - STAMBENI OBJEKTI
- PLANIRANI POSLOVNI OBJEKTI
- DIPLOMATSKO - KONZULARNO PREDSTAVNIŠTVO
- DOGRADNJA - MAŠINSKI FAKULTET
- UREĐENE ZELENE POVRŠINE
- UREĐENE JAVNE POVRŠINE
- PLANIRANE SAOBRAĆAJNICE

Broj parcele	Funkcija	Površina parcele	Tlocrtna površina	BGP	Procenat izgrađenosti	Koeficijent izgrađenosti	Maksimalna visina
1.	Poslovno-stambeni	15.200m2	5.900m2	56.600m2	39	3,7	50m
2.	Poslovno-stambeni	2.175m2	1.180m2	11.520m2	54,25	5,3	50m
3.	Poslovno-stambeni	2.280m2	2.080m2	8.480m2	91	3,7	50m
4.	Diplomatsko-konzularno predstavništvo	5.100m2	2.160m2	6.475m2	42,4	1,27	21m
5.	Muzej Ars Aevi	7.350m2	2.996m2	6.250m2	40	0,85	x
6.	Poslovni objekat	1.518m2	1.418m2	5.600m2	93,5	3,7	21m
7.	Poslovni objekat	515m2	515m2	1.900m2	100	3,7	21m

ELABORAT:

FAZA:

SADRŽAJ:

GRADONAČELNIK GRADA SARAJEVO

REGULACIONI PLAN "KVADRANT C - MARIJIN DVOR"

URBANIZAM

URBANISTIČKO REŠENJE RAZMJJEŠTAJ, NAMJENA I SPRATNOST OBJEKATA

RAZMJJERA:

DIMENZIJU:

DATUM:

BROJ PRILOGA:

1:1000

(1.05 x 0.5) m2

11 / 2025

7.